



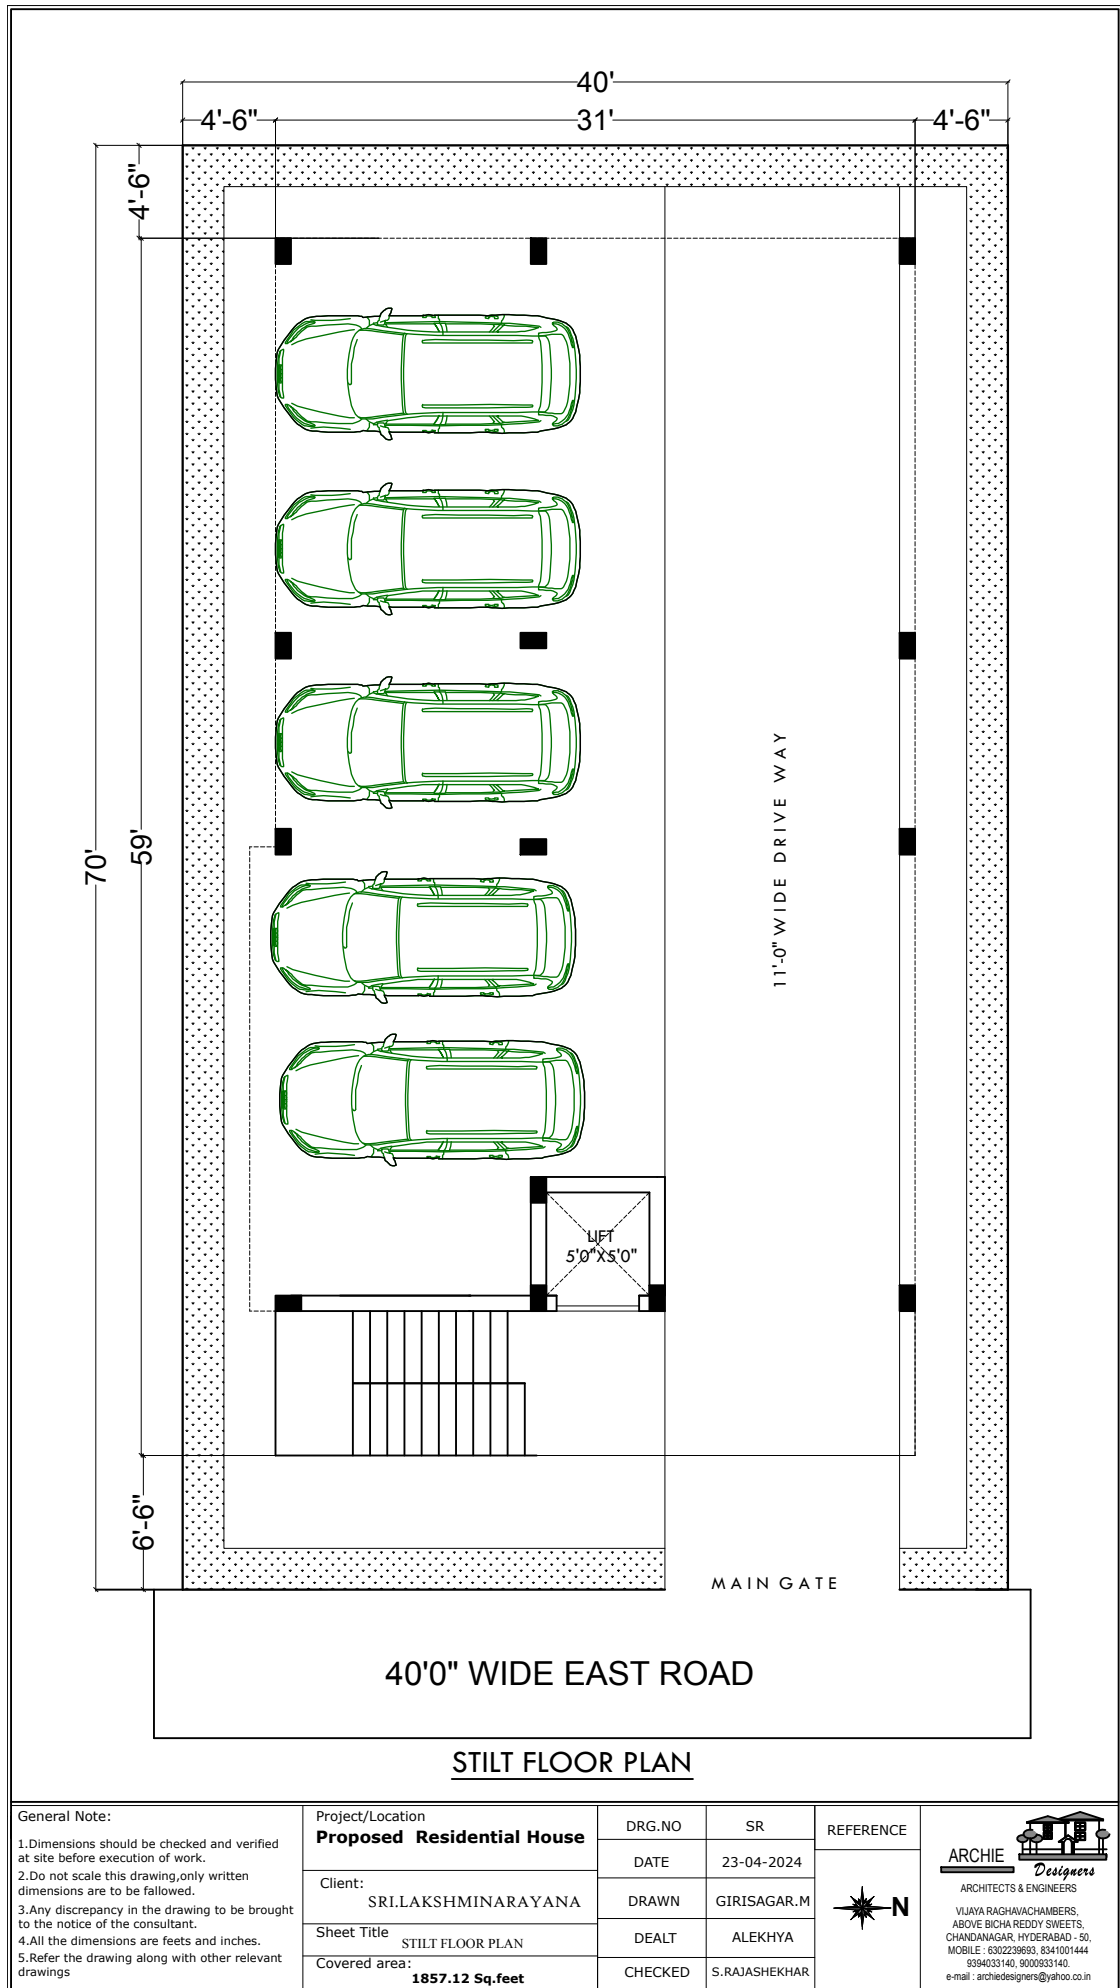

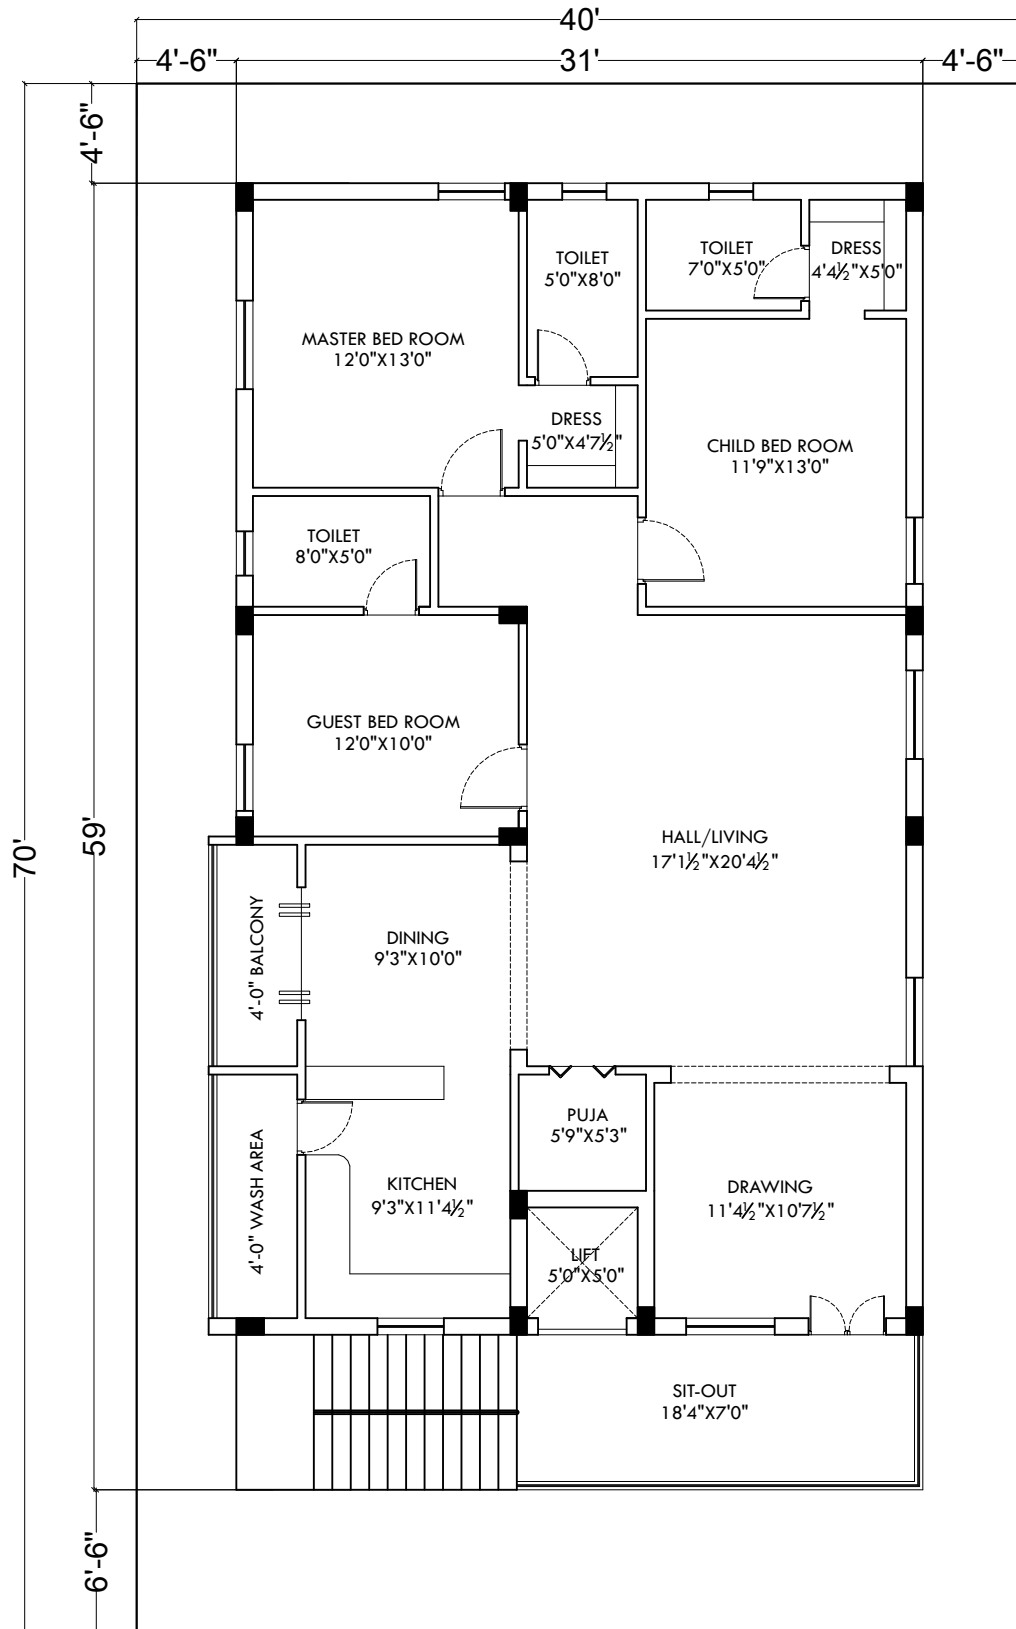

TYPICAL FLOOR PLAN

General Note:

1. Dimensions should be checked and verified at site before execution of work.
2. Do not scale this drawing, only written dimensions are to be followed.
3. Any discrepancy in the drawing to be brought to the notice of the consultant.
4. All the dimensions are feet and inches.
5. Refer the drawing along with other relevant drawings

Project/Location

Proposed Residential House

Client:

SRI.LAKSHMINARAYANA

Sheet Title

TYPICAL FLOOR PLAN

Covered area:

1857.12 Sq.feet

DRG.NO

DATE

DRAWN

DEALT

CHECKED

SR

23-04-2024

GIRISAGAR.M

ALEKHYA

S.RAJASHEKHAR

REFERENCE




ARCHIE



ARCHITECTS & ENGINEERS

VIJAYA RAGHAVACHAMBERS,
ABOVE BICHA REDDY SWEETS,
CHANDANAGAR, HYDERABAD - 50,
MOBILE : 8302239893, 8341001444
9394033140, 9000933140
e-mail : archiedesigners@yahoo.co.in

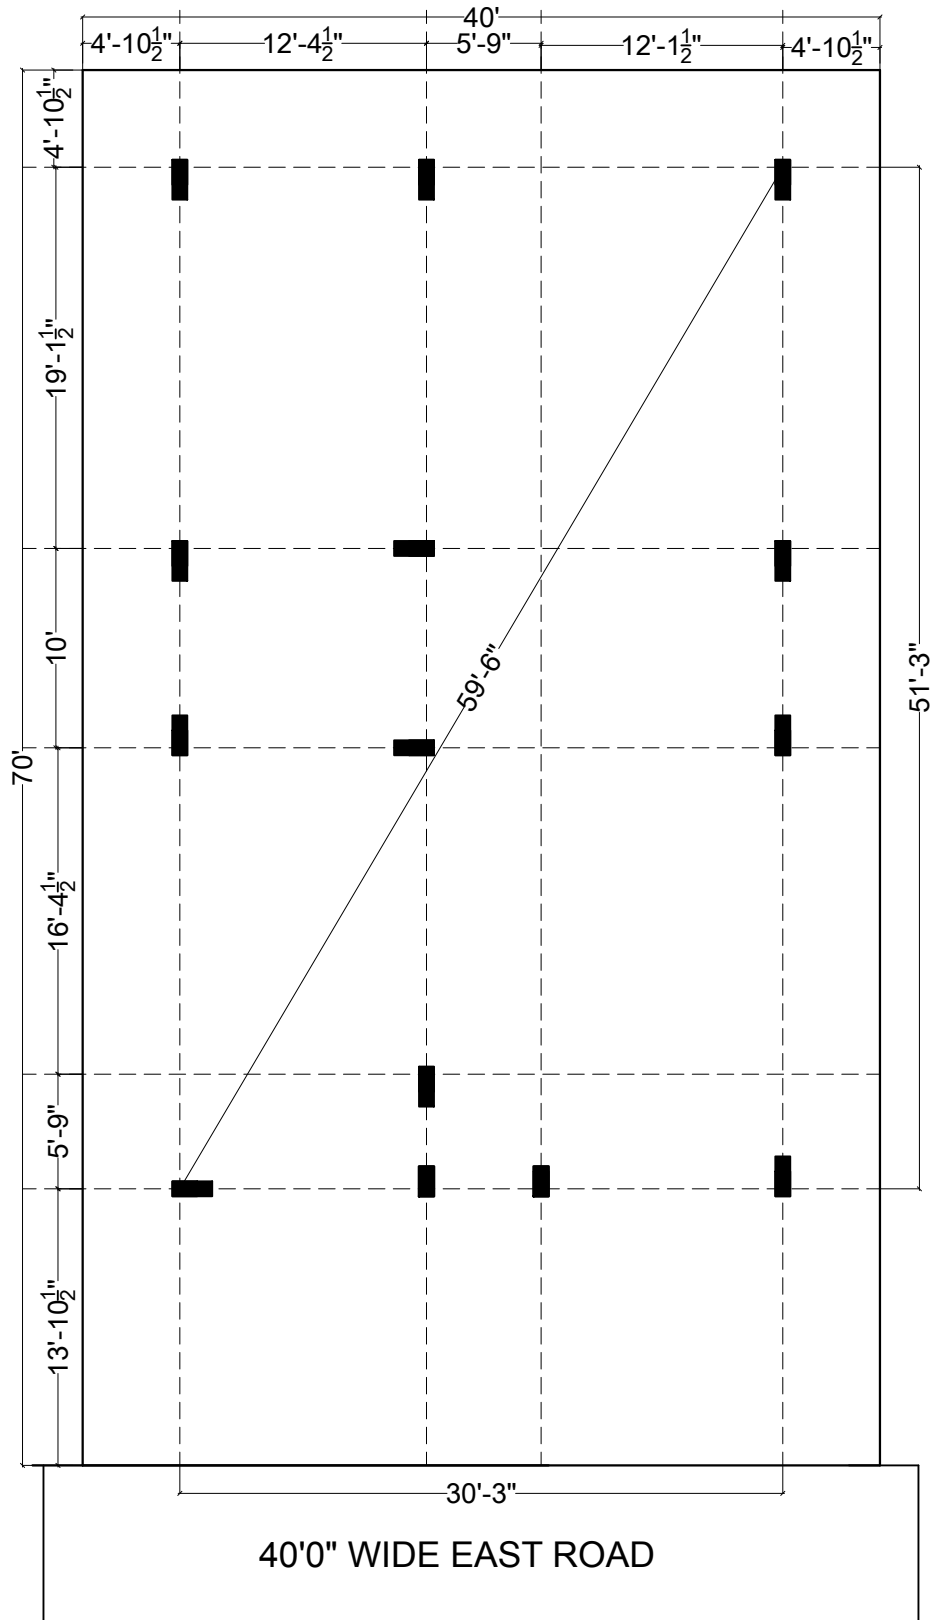

General Note:

1. Dimensions should be checked and verified at site before execution of work.
2. Do not scale this drawing, only written dimensions are to be followed.
3. Any discrepancy in the drawing to be brought to the notice of the consultant.
4. All the dimensions are feet and inches.
5. Refer the drawing along with other relevant drawings

Project/Location

Proposed Residential House

Client:

SRI.LAKSHMINARAYANA

Sheet Title

STILT FLOOR PLAN

Covered area:

1857.12 Sq.feet

DRG.NO

DATE

DRAWN

DEALT

CHECKED

SR

23-04-2024

GIRISAGAR.M


ALEKHYA

S.RAJASHEKHAR

REFERENCE



ARCHIE 
Designers
 ARCHITECTS & ENGINEERS
 VIJAYA RAGHAVACHAMBERS,
 ABOVE BICHA REDDY SWEETS,
 CHANDANAGAR, HYDERABAD - 50,
 MOBILE : 6302239693, 8341001444
 9394033140, 9000933140
 e-mail : archiedesigners@yahoo.co.in

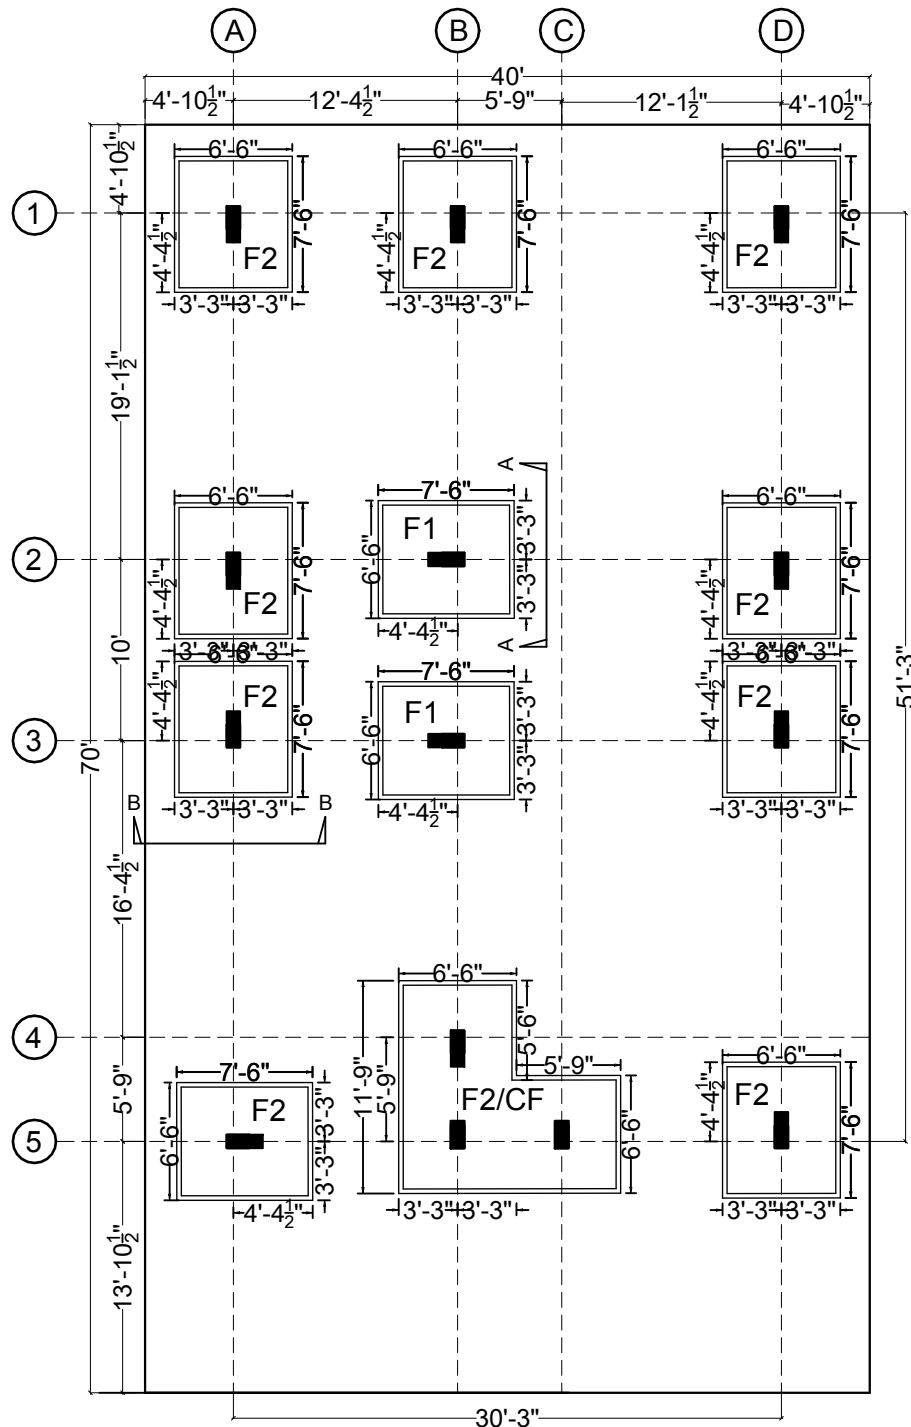

SPECIFICATIONS FOR R.C.C.WORK.

(UNLESS OTHERWISE SPECIFIED)

- 1) FOOTING ARE CONCENTRIC WITH COLUMNS.
- 2) STANDARD G.I./RUBBER/PVC WATER STOPS SHOULD BE PROVIDE AT ALL CONSTRUCTIONS JOINT IN WALLS/RAFTS.
- 3) USE CONCRETE M20 AND HIGH STRENGTH RIBBED TOR STEEL WITH YY 415 N/mm²
- 4) DEFORMED REINFORCEMENT SHALL CONFORM IS 1786 / 1789.
- 5) MILD STEEL REINFORCEMENT SHALL CONFORM TO IS 1786 / 1789.
- 6) M.S PLAIN BARS SHALL HAVE GURANTEED YIELD STRESS.
- 7) MINIMUM CLEAR COVER TO MAIN STEEL TO BE AS FOLLOWS, FOOTINGS : 50MM; COLUMNS : 40MM; PEDASTAL:90MM; BEAMS:25MM AND SLABS:15MM.
- 8) DEVELOPMENT LENGHT FOR DEFORMED STEEL AS FOLLOWS.
1) 8MM:40CM 2) 10MM:50CM 3) 12MM:60CM
4) 16MM:75CM 2) 20MM:100CM 3) 25MM:120CM
- 9) EX-EXTRA CR-CURTAIL ST-STRAIGHT.
- 10) PROVEDE 25MM CAMBER AT FREE AND FOR CANTILEVER BEAMS & SLABS.
- 11) IN SLAB CRANK POSITIVE STEEL AT 1/3 TH SPAN. AND EXTEND NEGATIVE STEEL UP TO 1/3 TH SPAN.

GENERAL NOTES

(UNLESS OTHERWISE SPECIFIED)

- 1) ALL DIMENSIONS ARE IN MM.
- 2) S.B.C OF SOIL IS TAKEN AS 30 T/SQ.M. AT DEPTH OF 2000MM BELOW N.G.L.
- 3) DISCREPANCY IN DRAWING IF ANY SHALL BE BROUGHT TO THE NOTICE OF THE SITE ENGINEER/CONSULTING ENGINEER.
- 4) DO NOT SCALE THE DRG. FOLLOW WRITTEN DIMENSIONS ONLY.
- 5) READ THE DRG. ALONG WITH ARCH. DRG.

NOTE:-

COLUMN CENTRE LINE REF. WITH WALL CENTRE



DATE:

23.04.2024

CHECK:

S. RAJASHEKHAR

ORIENTATION

DRG. BY.

K.RAMESH



TITLE:

CENTRELINE EXCAVATION SIZES

CLIENT:

SRI.LAKSHMINARAYANA


ARCHITECT.

S. RAJASHEKHAR
CONSULTANT




ARCHIE
Designers
ARCHITECTS & ENGINEERS


FIRST FLOOR , OFFICE NO.1-15/1/217, ABOVE BICHA REDDY SWEETS , VIJAYA RAGHAVA CHAMBERS , NEAR B.H.E.L , CHANDANAGAR , HYDERABAD - 500050 , TELANGANA STATE., OFFICE PH. NO'S : 23033140, 23031352, 65573140., MOBILE : 9394033140, 9000933140, 9849018962., e-mail : archiedesigners@yahoo.co.in

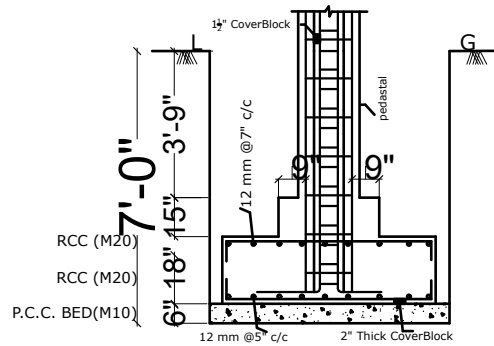


FOOTING F1(SECTION A-A)

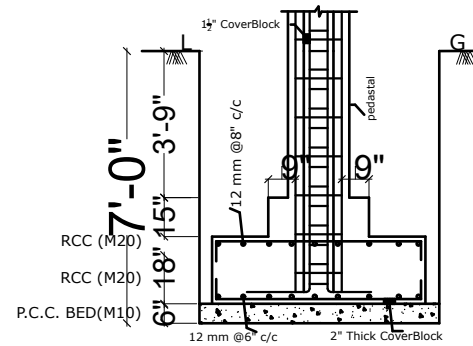

FOOTING F2(SECTION B-B)

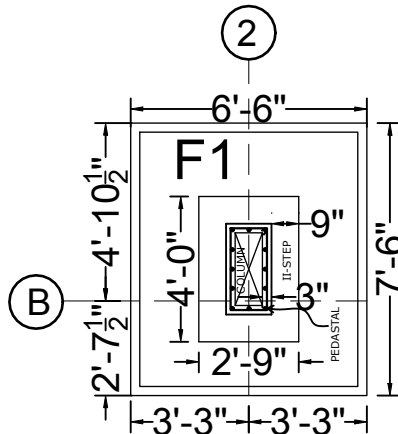

FOOTING F1(PLAN)

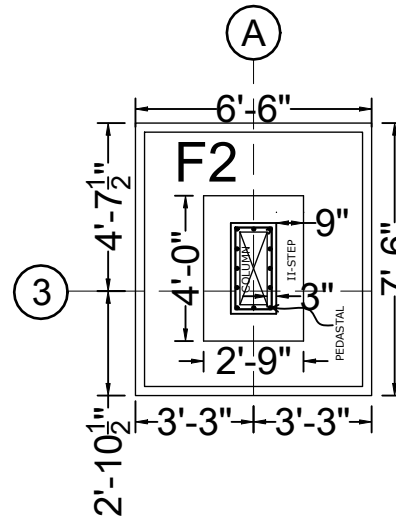

FOOTING F2(PLAN)

FOOTING DETAILS (F1)

FOOTING DETAILS (F2)

- 1) FOOTING ARE CONCENTRIC WITH COLUMNS.
- 2) STANDARD G.I./RUBBER/PVC WATER STOPS SHOULD BE PROVIDE AT ALL CONSTRUCTIONS JOINT IN WALLS/RAFTS.
- 3) USE CONCRETE M25 AND HIGH STRENGTH RIBBED TOR STEEL WITH YY 500 N/mm
- 4) DEFORMED REINFORCEMENT SHALL CONFORM IS 1786 / 1789.
- 5) MILD STEEL REINFORCEMENT SHALL CONFORM TO IS 1786 / 1789.
- 6) M.S PLAIN BARS SHALL HAVE GURANTEED YIELD STRESS.
- 7) MINIMUM CLEAR COVER TO MAIN STEEL TO BE AS FOLLOWS, FOOTINGS : 50MM; COLUMNS :40MM; PEDASTAL:90MM; BEAMS:25MM AND SLABS:15MM.
- 8) DEVELOPMENT LENGHT FOR DEFORMED STEEL AS FOLLOWS.
 - 1) 8MM:40CM 2) 10MM:50CM 3) 12MM:60CM
 - 4) 16MM:75CM 2) 20MM:100CM 3) 25MM:120CM
- 9) EX-EXTRA CR-CURTAIL ST-STRAIGHT.
- 10) PROVEDE 25MM CAMBER AT FREE AND FOR CANTILEVER BEAMS & SLABS.
- 11) IN SLAB CRANK POSITIVE STEEL AT $\frac{1}{3}$ TH SPAN. AND EXTEND NEGATIVE STEEL UP TO $\frac{1}{4}$ TH SPAN.

DATE:		NORTH
23.04.2024		
CHECK:	DRG. BY.	
S. RAJASHEKHAR	K.RAMESH	
TITLE:		
FOOTING DETAILS		
CLIENT:		
SRI.LAKSHMINARAYANA		COVERED
ARCHITECT.		



S. RAJASHEKHAR
CONSULTANT



ARCHIE
Designers
ARCHITECTS & ENGINEERS

FIRST FLOOR , OFFICE NO.1-15/1/217, ABOVE
BICHA REDDY SWEETS , VIJAYA RAGHAVA
CHAMBERS , NEAR B.H.E.L , CHANDANAGAR ,
HYDERABAD - 500050 , TELANGANA STATE.,
OFFICE PH. NO'S : 23033140, 23031352, 65573140.,
MOBILE : 9394033140, 9000933140, 9849018962.,
e-mail : archiedesigners@yahoo.co.in

STAIR CASE DETAIL

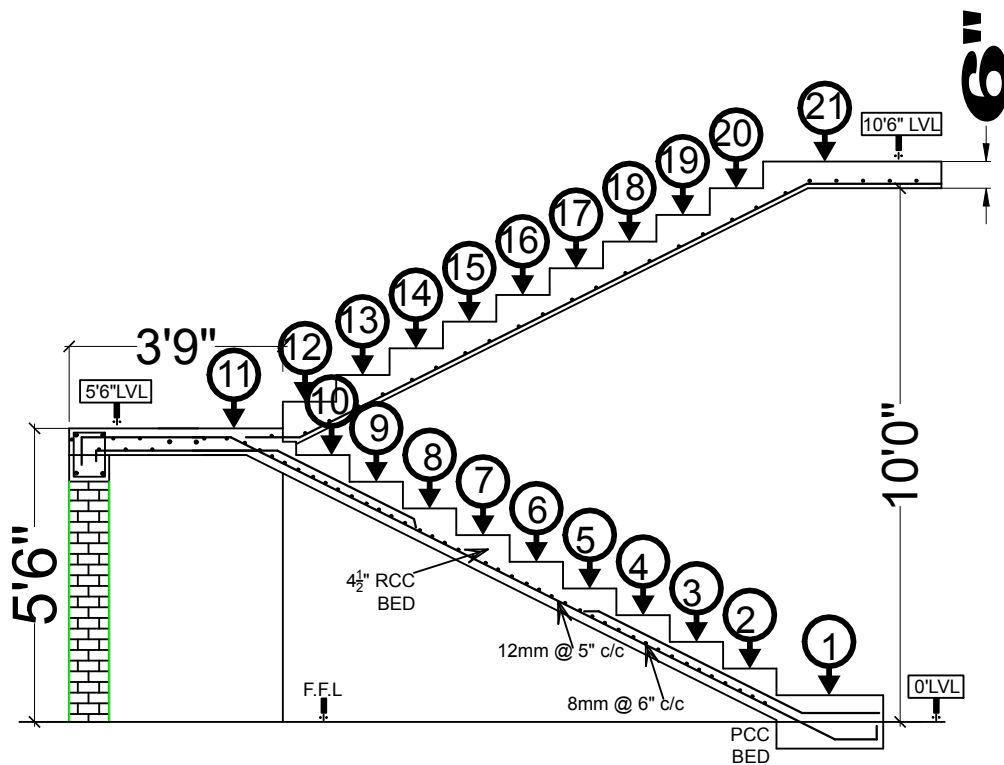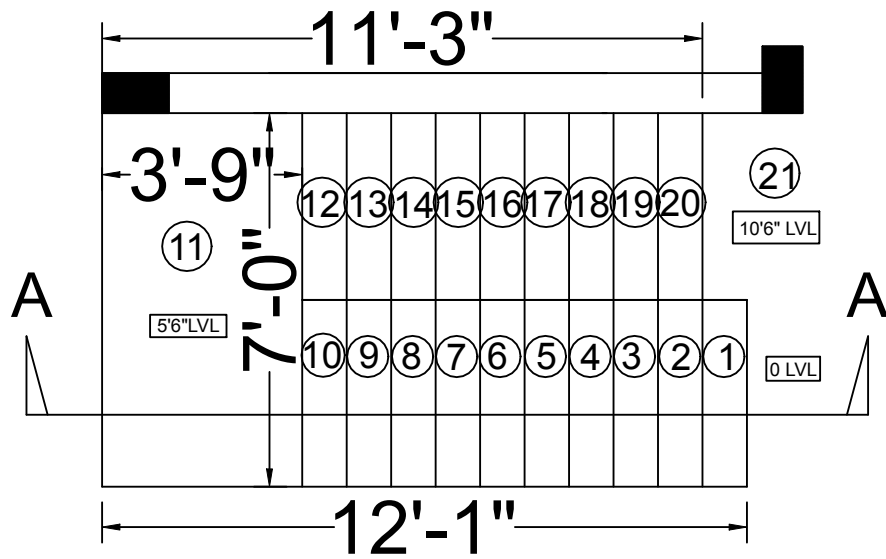

SECTION AT(A-A)

RISER HIGHT - 6"

TREAD LENTH- 10"

SRI.LAKSHMINARAYANA